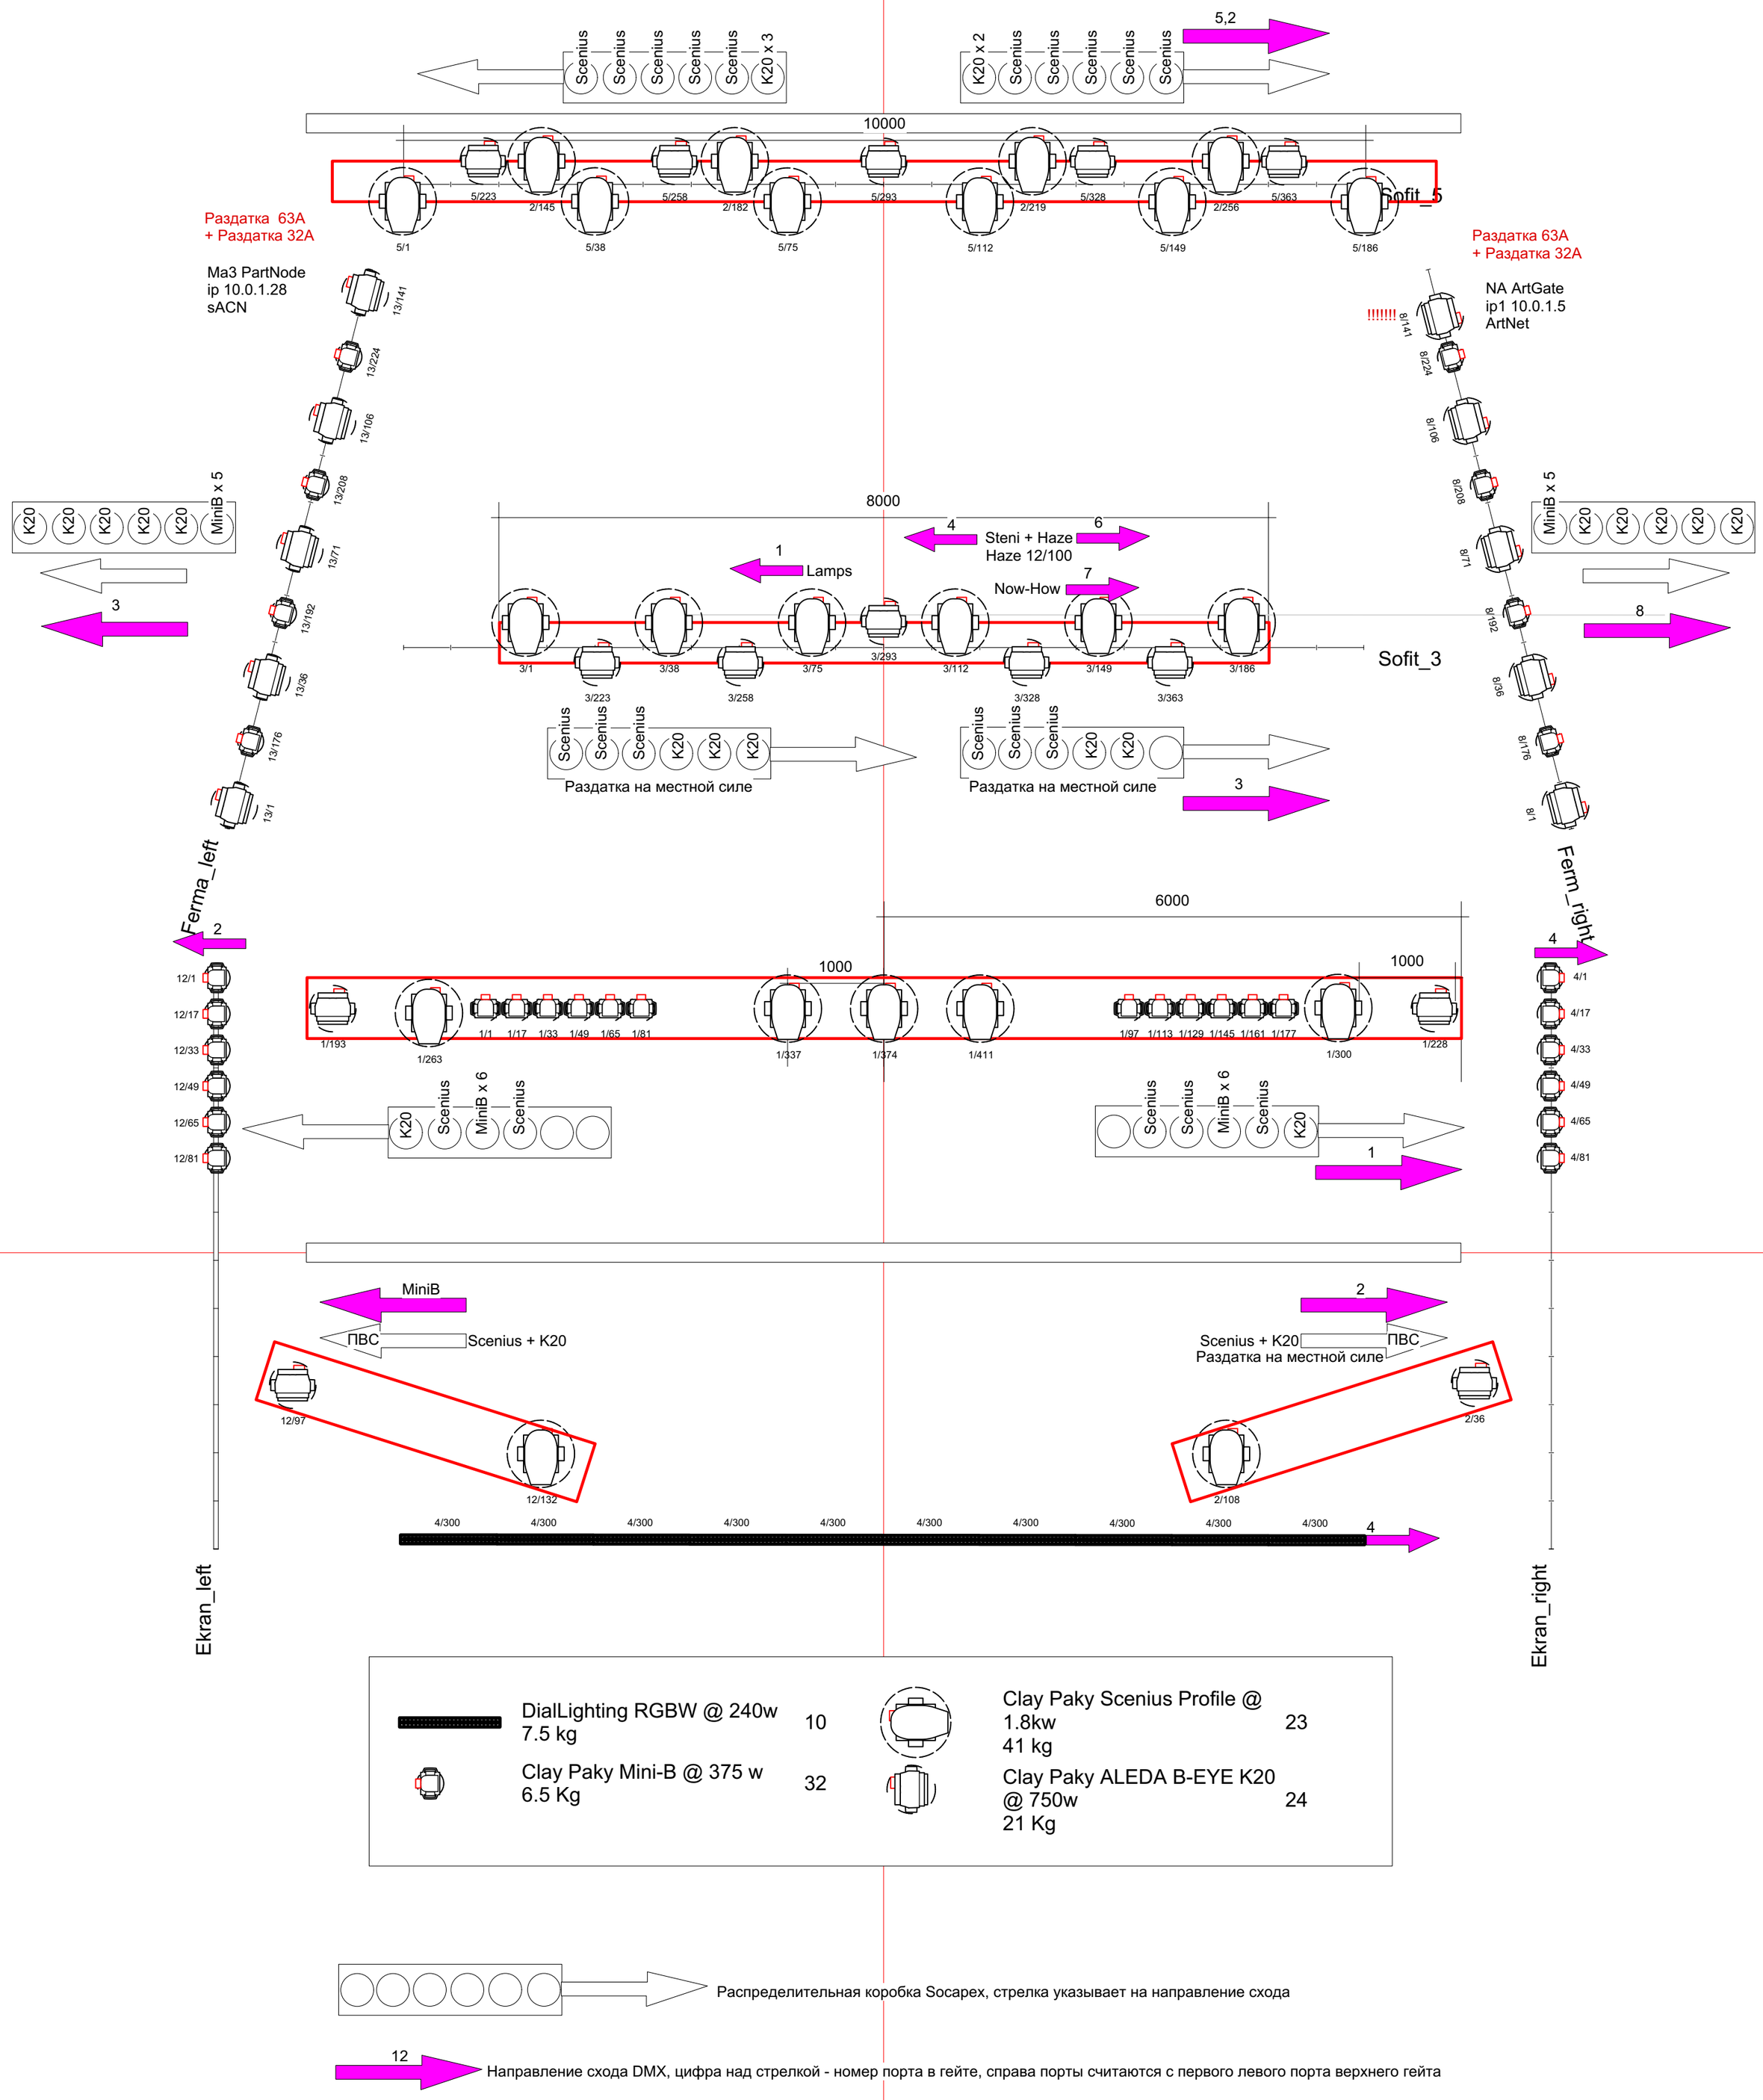
Scenius
K20 x 3
K20 x 2
5,2
10000
Sofit_5
5/1
5/38
5/75
5/112
5/149
5/186
5/223
2/145
5/258
2/182
5/293
2/219
5/328
2/256
5/363
Раздатка 63A
+ Раздатка 32A
Ma3 PartNode
ip 10.0.1.28
sACN
13/141
13/224
13/106
13/208
13/71
13/192
13/36
13/176
13/1
MiniB x 5
K20
3
Раздатка 63A
+ Раздатка 32A
NA ArtGate
ip1 10.0.1.5
ArtNet
!!!!!!!
8/141
8/224
8/106
8/208
8/71
8/192
8/36
8/176
8/1
8
8000
4
6
Steni + Haze
Haze 12/100
1
Lamps
7
Now-How
3/1
3/38
3/75
3/293
3/112
3/149
3/186
3/223
3/258
3/328
3/363
Sofit_3
Раздатка на местной силе
Раздатка на местной силе
3
Ferma_left
Ferm_right
2
4
6000
1000
1000
12/1
12/17
12/33
12/49
12/65
12/81
1/193
1/263
1/1
1/17
1/33
1/49
1/65
1/81
1/337
1/374
1/411
1/97
1/113
1/129
1/145
1/161
1/177
1/300
1/228
4/1
4/17
4/33
4/49
4/65
4/81
K20
Scenius
MiniB x 6
1
MiniB
ПВС
Scenius + K20
12/97
12/132
2
Scenius + K20
ПВС
Раздатка на местной силе
2/36
2/108
4/300
4
Ekran_left
Ekran_right
DialLighting RGBW @ 240w
7.5 kg
10
Clay Paky Mini-B @ 375 w
6.5 Kg
32
Clay Paky Scenius Profile @
1.8kw
41 kg
23
Clay Paky ALEDA B-EYE K20
@ 750w
21 Kg
24
Распределительная коробка Socapex, стрелка указывает на направление схода
12
Направление схода DMX, цифра над стрелкой - номер порта в гейте, справа порты считаются с первого левого порта верхнего гейта