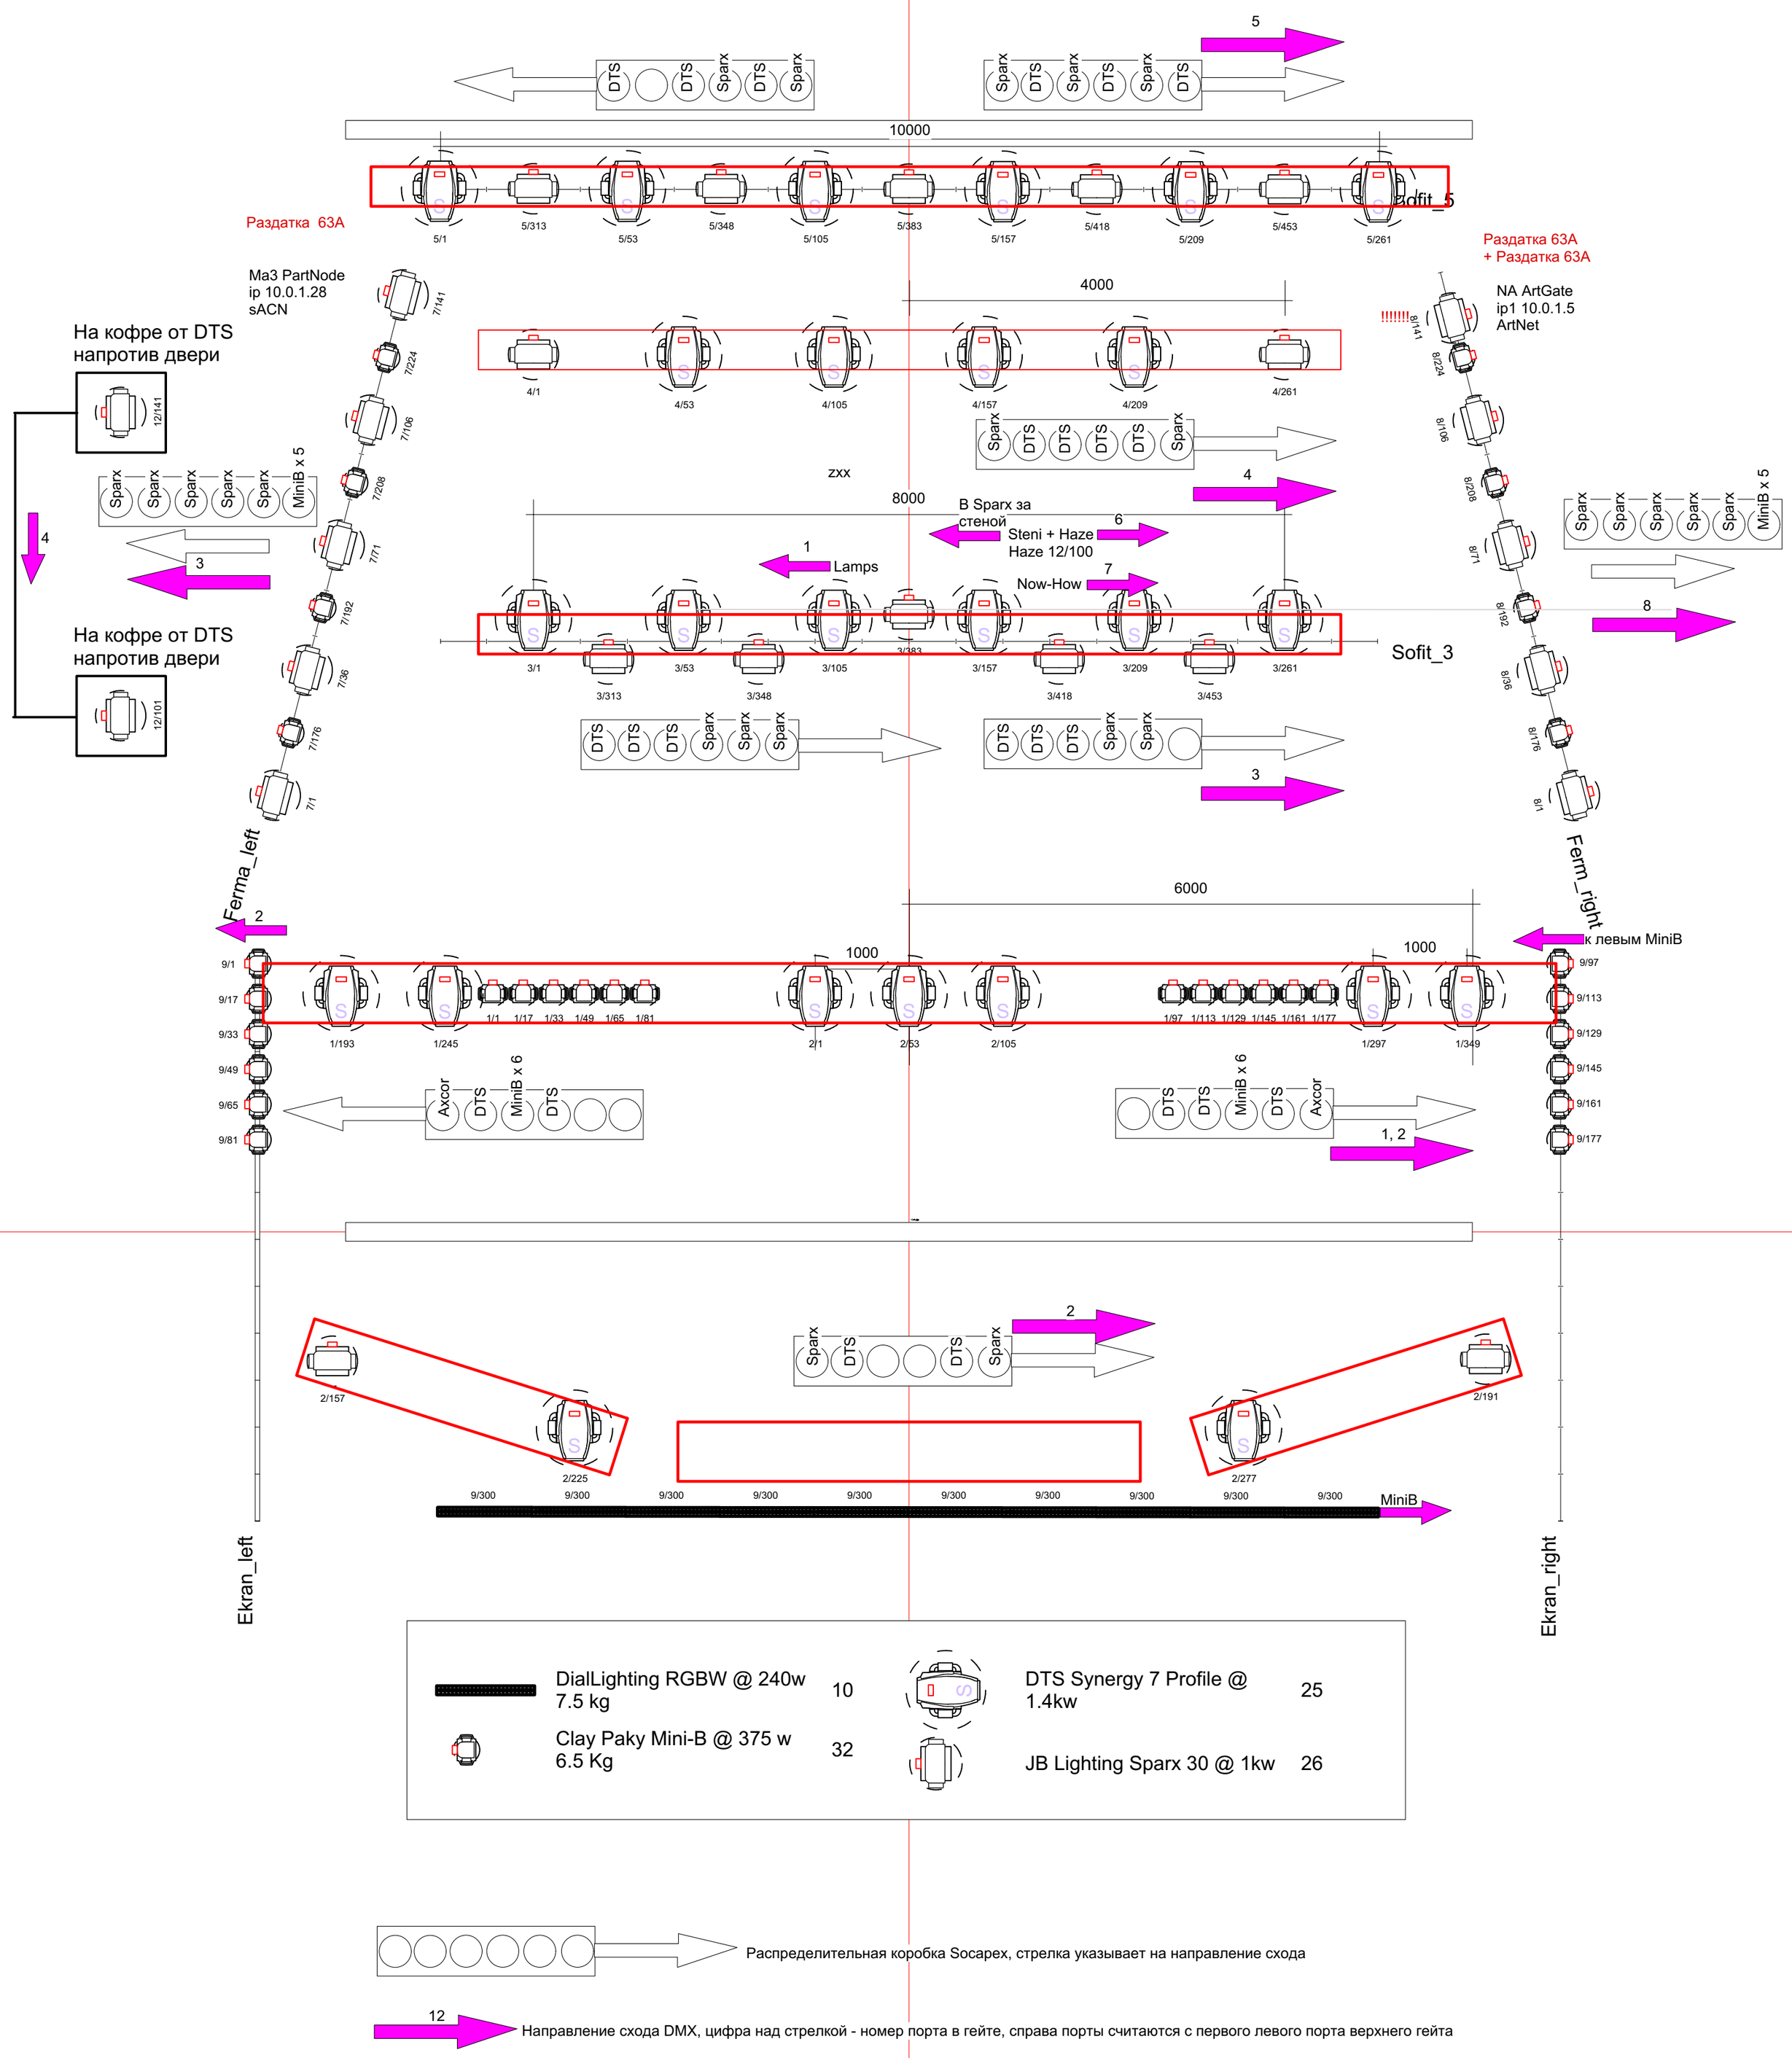
10000
Раздатка 63A
Sofit_5
5/1
5/313
5/53
5/348
5/105
5/383
5/157
5/418
5/209
5/453
5/261
Раздатка 63A
+ Раздатка 63A
Ma3 PartNode
ip 10.0.1.28
sACN
NA ArtGate
ip1 10.0.1.5
ArtNet
!!!!!!!
4000
4/1
4/53
4/105
4/157
4/209
4/261
На кофре от DTS
напротив двери
12/141
MiniB x 5
zxx
8000
В Sparx за
стеной
Steni + Haze
Haze 12/100
Lamps
Now-How
Sofit_3
3/1
3/53
3/105
3/383
3/157
3/209
3/261
3/313
3/348
3/418
3/453
На кофре от DTS
напротив двери
12/101
Ferma_left
Ferm_right
6000
1000
1000
к левым MiniB
1/193
1/245
1/1
1/17
1/33
1/49
1/65
1/81
2/1
2/53
2/105
1/97
1/113
1/129
1/145
1/161
1/177
1/297
1/349
Axcor
DTS
MiniB x 6
2/157
2/225
2/277
2/191
9/300
MiniB
Ekran_left
Ekran_right
DialLighting RGBW @ 240w
7.5 kg
10
DTS Synergy 7 Profile @
1.4kw
25
Clay Paky Mini-B @ 375 w
6.5 Kg
32
JB Lighting Sparx 30 @ 1kw
26
Распределительная коробка Socapex, стрелка указывает на направление схода
Направление схода DMX, цифра над стрелкой - номер порта в гейте, справа порты считаются с первого левого порта верхнего гейта